

1 ROZWINIĘCIE BLACHY — po wycięciu, przed gięciem skala 1:10

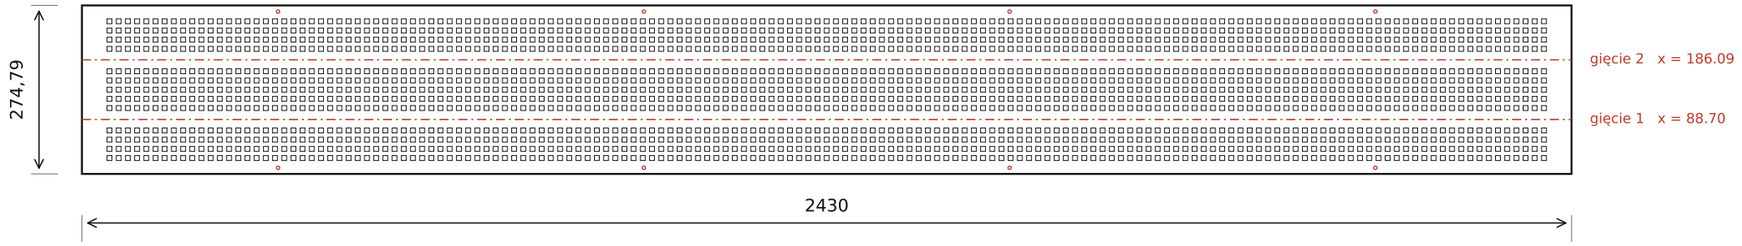


Czerwona kreska-kropka = linia gięcia (w pliku DXF jej nie ma). Czerwone okręgi = otwory montażowe ø5,5 przy krawędziach dochodzących do ściany.
Warstwa cięcia w DXF: CIECIE (jedyna), wszystkie kontury zamknięte.

2 PRZEKRÓJ PO GIĘCIU — widok z góry skala 1:1

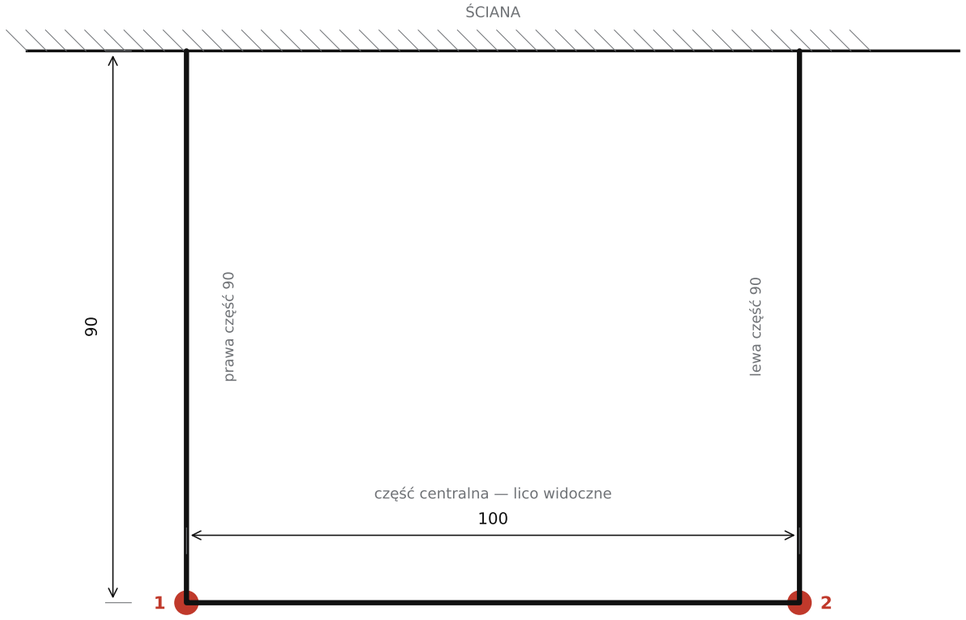


Dwa gięcia po 90°, promień wewnętrzny R1,5 mm, oba w tę samą stronę.
Forma Π wg specyfikacji: centralna 100 mm, prawa i lewa po 90 mm.
Gabaryt po gięciu: 100 × 90 × 2430 mm (szer. × głęb. × wys.).

3 KĄTOWNIK MONTAŻOWY — 8 szt. skala 1:1

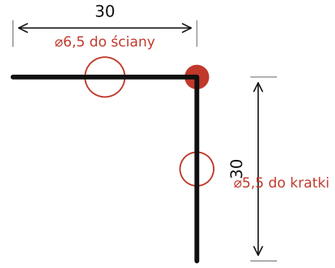

DC01 2,0 mm, rozwinięcie 56.52 × 80 mm,
jedno gięcie 90° w x = 28.26, R wewn. 2,0 mm.
Po 4 szt. na każdą krawędź, ukryte wewnątrz obudowy.

4 DETAL PERFORACJI skala 1:1

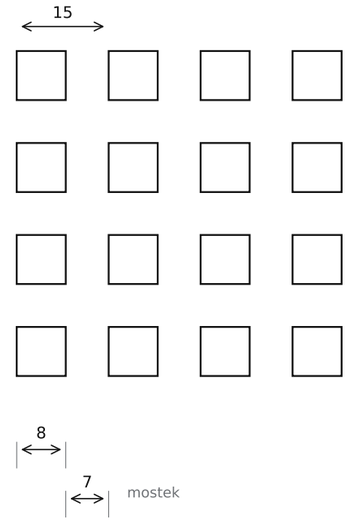

Otwory kwadratowe 8 × 8 mm, podziałka 15 mm w obu osiach.
Mostek 7 mm = 4,7 × grubości blachy. Powierzchnia otwarta 29 %.
Kolumny: 4 (bok) + 5 (centralna) + 4 (bok) × 157 rzędów = 2041 otworów.
Perforacja kończy się 13,9 mm przed każdym narożem — gięcie jej nie deformuje.

5 KOLEJNOŚĆ GIĘCIA

nr	element	linia x [mm]	kąt	kierunek
1	naroże prawe	88.70	90°	ten sam dla obu
2	naroże lewe	186.09	90°	ten sam dla obu

Oba gięcia w tę samą stronę — detalu nie trzeba obracać ani przezbrajać prasy.
Kolejność dowolna; wygodniej najpierw prawe naroże, potem lewe.
R wewnętrzny 1,5 mm · K = 0,44 · odcięcie na gięcie 2,607 mm.
Przy innym K-factorze prasy rozwinięcie trzeba przeliczyć.

6 UWAGI

Forma Π zgodna ze specyfikacją konstrukcyjną zamawiającego:
wysokość 2430 mm, centralna 100 mm, prawa i lewa część po 90 mm.
Wszystkie trzy płaszczyzny perforowane. Jeden element gięty.
Materiał: DC01, grubość 1,5 mm (kątowniki 2,0 mm).
Wykończenie: odgratowanie, odtłuszczenie, malowanie proszkowe na biało RAL 9003 — również wewnątrz otworów.
Montaż: krawędzie boczne przykręcane do 8 kątowników zamocowanych do ściany. Na glazurze nie widać żadnego mocowania.
Cięcie 70,9 m, 2050 przebić. Masa 6,32 kg. Arkusz 1250 × 2500: 4 szt.
Prasa krawędziowa musi mieć długość roboczą min. 2430 mm.

ULAMEX · Zawada 144 · 97-200 Tomaszów Mazowiecki

KRATKA Π — OBUDOWA PIONU INSTALACYJNEGO

Materiał DC01, gr. 1,5 mm (+ kątowniki 2,0)	Nr rysunku ULX-2430-DC01-03
Wykończenie malowanie proszkowe RAL 9003	Ilość / jednostki 1 kpl. · wymiary w mm
Masa 6,32 kg + 8 × 0,07 kg	Tolerancje ogólne / data ISO 2768-mK · 2026-11-02